

P
O
R
T
F
O
L
I
O

À PROPOS

LEBOUCHER CLARA
claralbr@gmail.com

Étudiante en 2^e année à l'École de Condé en design d'espace, j'aime imaginer des espaces qui racontent quelque chose et dans lesquels on se sent bien. À travers mes projets, j'explore les volumes, les matières, la lumière et les usages tout en cherchant à trouver un équilibre entre esthétique et fonctionnalité. Ce portfolio présente mon parcours, mes recherches et les différentes façons dont j'apprends peu à peu à penser et à créer les espaces.

01	PROJET RÉSIDENTIEL PRIVÉ	projet personnel
02	40M2- L'INCONFORT	architecture d'intérieur
03	POP-UP LEGO	scénographie
04	L'ABRI DU VIDE	micro-architecture
05	PROJETS ANNUELS	travaux plastiques & expérimentations

01




PROJET RÉSIDENTIEL PRIVÉ

Dax, Nouvelle-Aquitaine

projet indépendant
été 2026

Pour ce projet au sein d'un domaine, l'objectif était d'imaginer l'aménagement complet de trois salles de bains en partant d'espaces totalement bruts.

En m'inspirant des besoins du client, j'ai cherché à concevoir des pièces simples et pratiques au quotidien. Le travail sur AutoCAD m'a permis d'organiser les volumes et de trouver la juste place pour chaque élément.

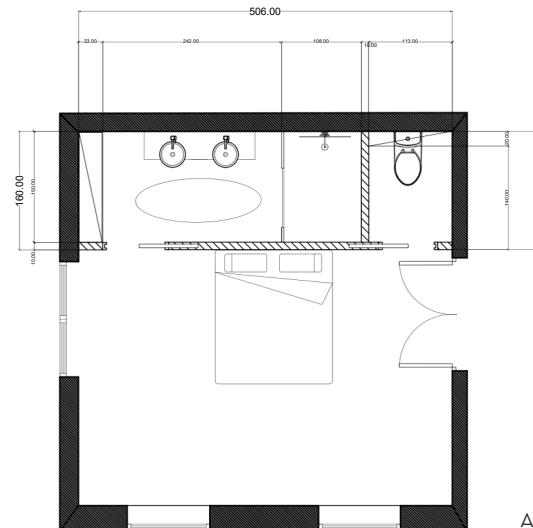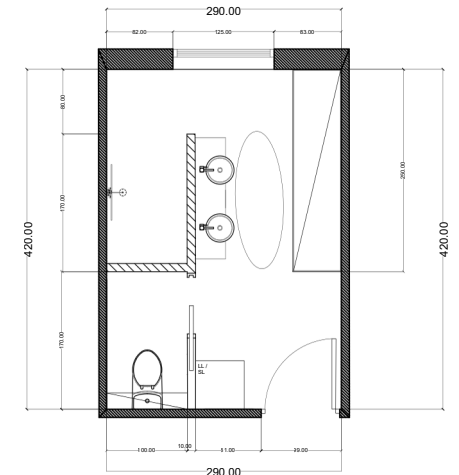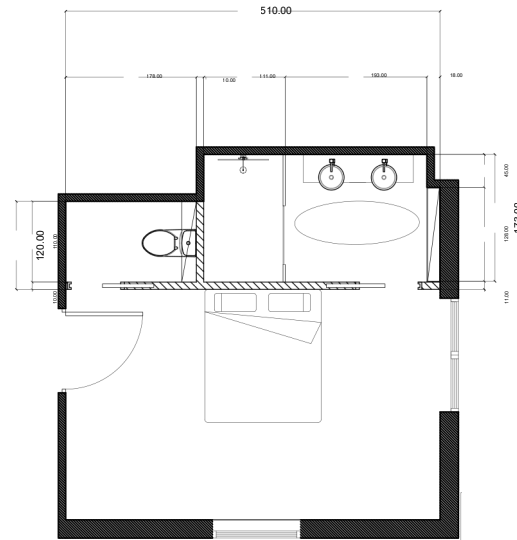

AUTOCAD

02

VIVRE, CRÉER, RÊVER

40 m²

projet scolaire

année 2026


Pour ce projet de 40 m², l'idée était d'imaginer un lieu fluide et bien optimisé pour pouvoir y vivre, créer et se détendre.

En partant de la demande du client, j'ai cherché à allier le côté pratique à une vraie sensibilité spatiale. J'ai alors pensé l'architecture d'intérieur afin qu'elle reflète l'univers du client, c'est-à-dire du dessin du mobilier au choix des matières où chaque détail permet de tourner les contraintes techniques en atouts.

PHOTOSHOP



Pour cela, j'ai imaginé des meubles qui s'adaptent aux contraintes de l'appartement pour optimiser chaque mètre carré sans encombrer. J'ai choisi des teintes douces pour capter la lumière naturelle et agrandir visuellement l'espace. Pour les matériaux, l'objectif était de combiner esthétique et solidité en utilisant des matières vivantes capables de résister à la vie de tous les jours.

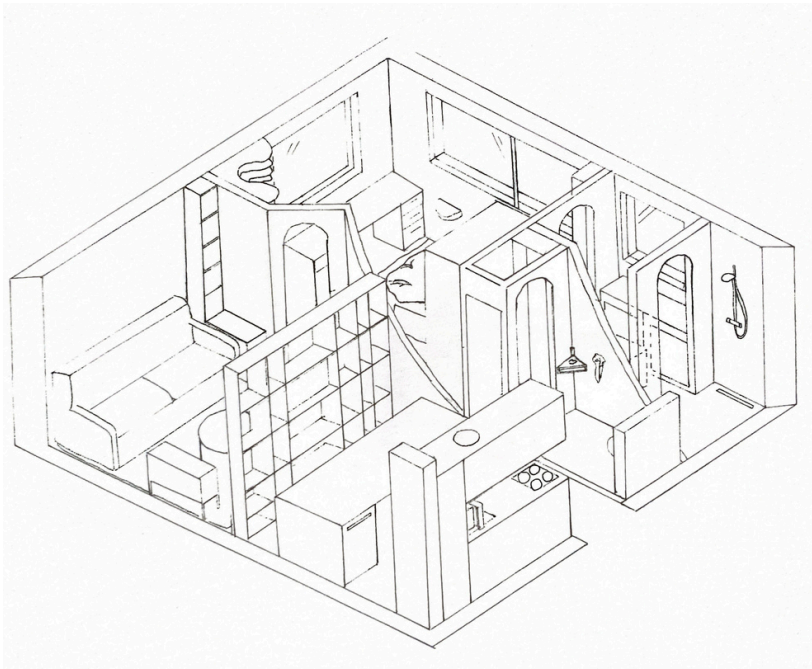

MAQUETTE

au 1/25ème



03



DE L'INCONFORT À UN CONFORT

Soutenance de projet de fin d'année





projet scolaire
année 2026

La démarche de ce projet est née en observant les limites du lieu actuel, notamment le manque de confort et la surcharge sensorielle. J'ai repensé le plan de la médiathèque en modifiant certains éléments de structure : l'objectif était de fluidifier les déplacements, améliorer le confort des usagers tout en mettant en valeur les volumes de l'espace existant.

AUTOCAD


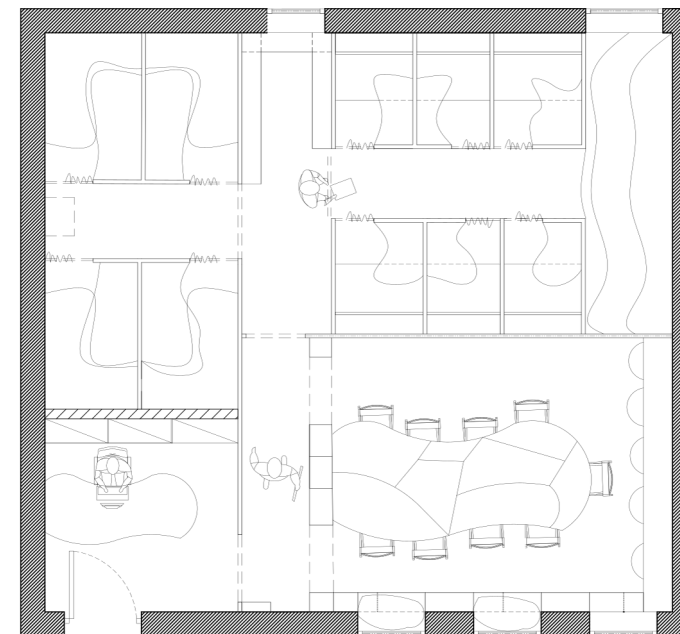
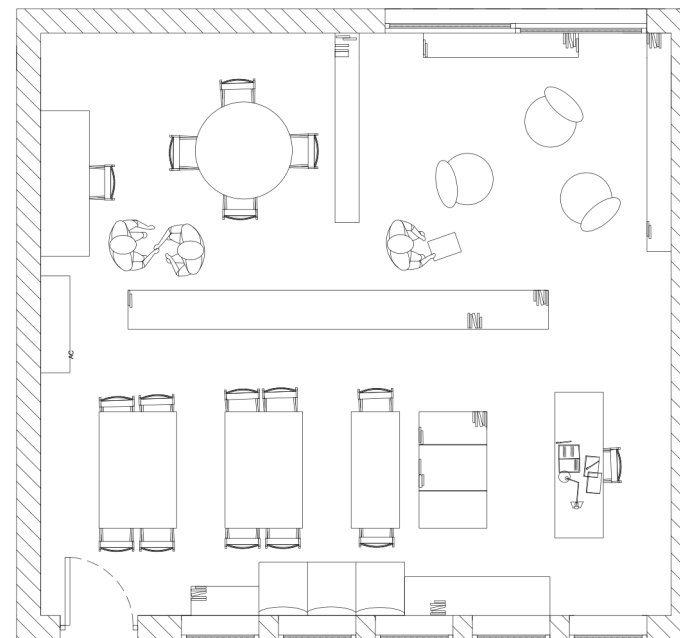


J'ai pensé cet aménagement comme un lieu chaleureux et apaisant, idéal pour le calme et la concentration. J'ai surtout travaillé sur l'acoustique, la gestion de la lumière et la création de petits espaces plus intimistes. Du dessin du mobilier aux détails d'assemblage, le projet remet le bien-être et le confort de l'utilisateur au centre, tout en gardant une vraie harmonie visuelle.

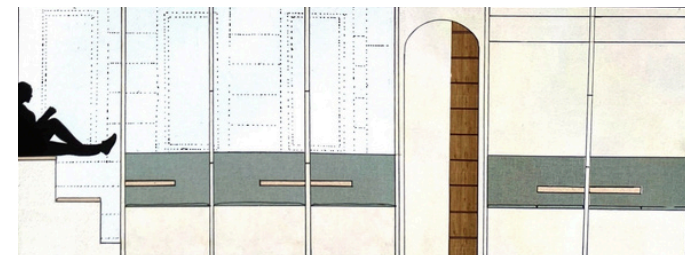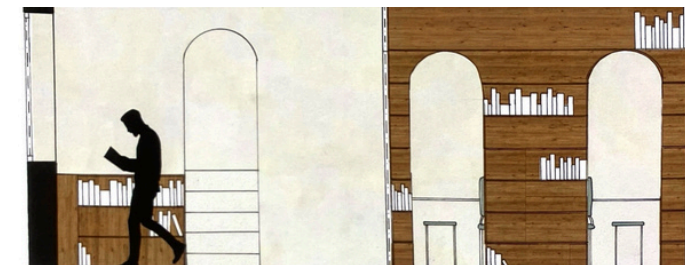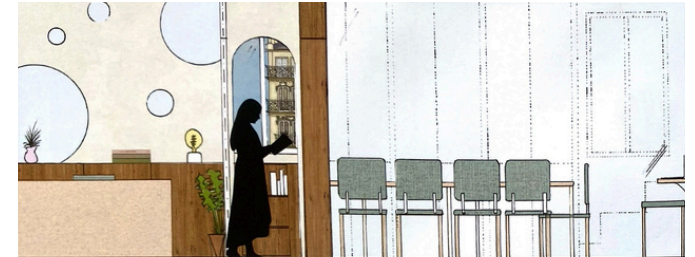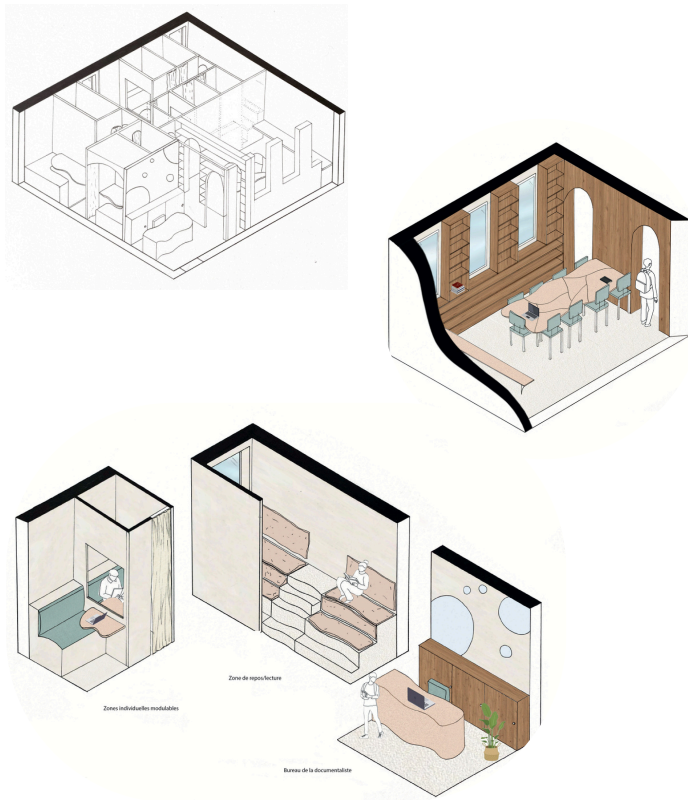

MAQUETTE

au 1/25ème et 1/50ème

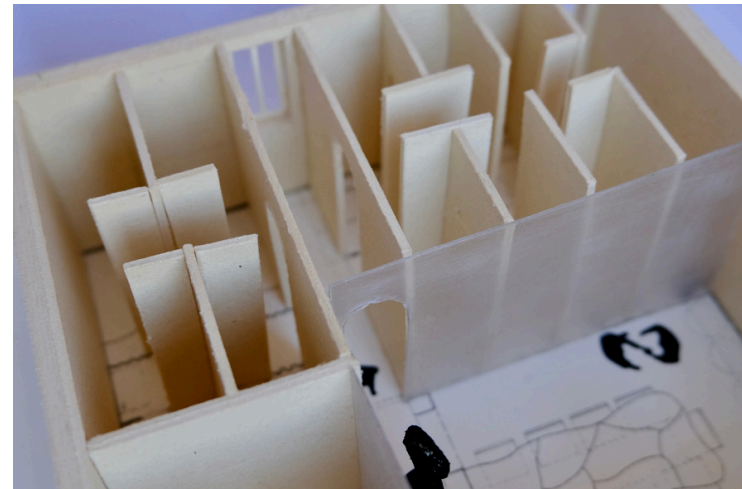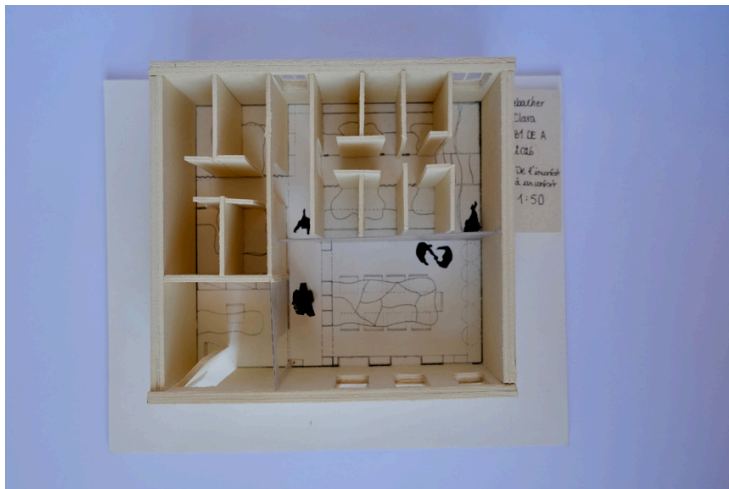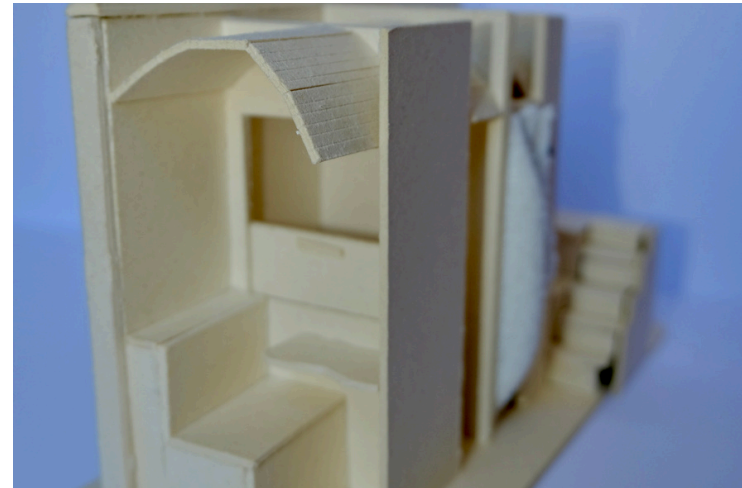


LEGO, CONSTRUIRE L'IMAGINAIRE

Projet en groupe

projet scolaire
année 2025

Pour ce projet de boutique éphémère autour du thème « LEGO : Construire l'imaginaire », on a voulu mettre l'accent sur le partage, la modularité et le plaisir de créer à tout âge. L'architecture reprend les formes géométriques de la marque pour créer un univers coloré et culturel. Dès l'entrée, un espace « musée » présente de grandes œuvres d'art réinventées en briques. Le parcours se prolonge ensuite très simplement avec un atelier interactif pour construire librement, un espace digital sur l'histoire de LEGO et une zone de vente.

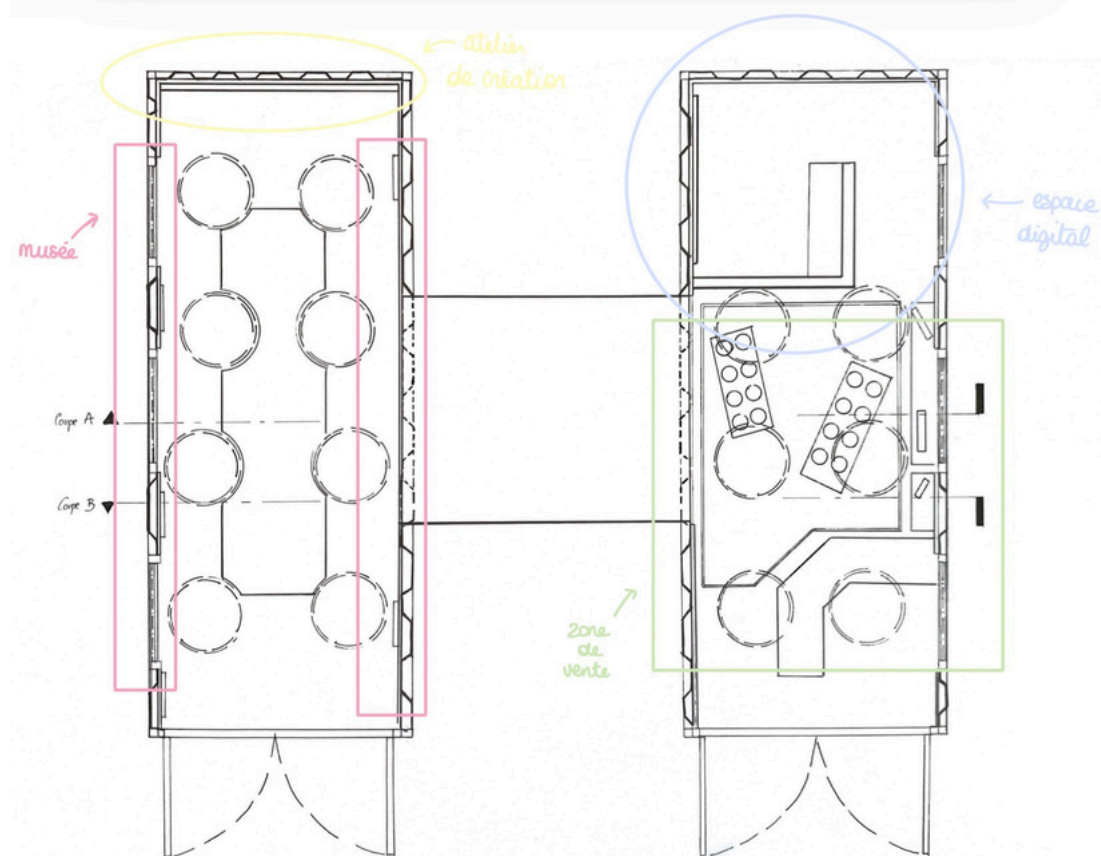

SCÉNOGRAPHIE
plan à la main

05




L'ABRI DU VIDE

Workshop

projet scolaire

année 2026

Réalisé en groupe pendant un workshop d'une semaine, ce projet de micro-architecture explore la notion de « l'abri du vide » inspirée par l'exposition “Constellations” de Michael Kenna. Notre travail s'est concentré sur les notions de reflets et disparition : placé en plein désert, le projet prend la forme d'un cube miroir entouré de panneaux orientables. Ouverts, les volets jouent avec la lumière et les teintes du verre ; fermés, ils reflètent le paysage à 360° pour faire disparaître totalement la structure dans son environnement.

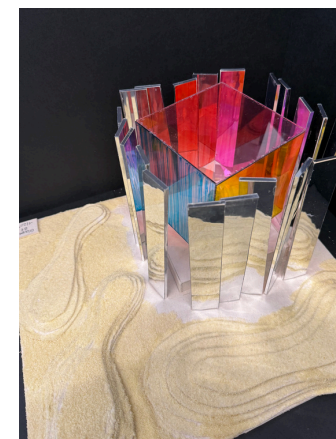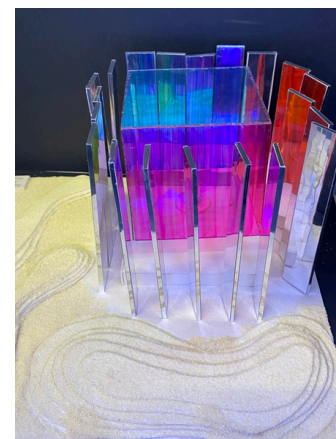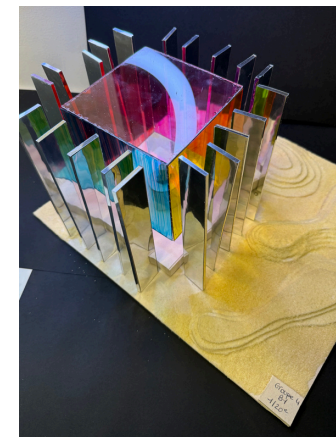



MICRO-ARCHITECTURE

06

TRAVAUX PLASTIQUES & EXPÉRIMENTATIONS

Plan d'une villa

projet scolaire
année 2026

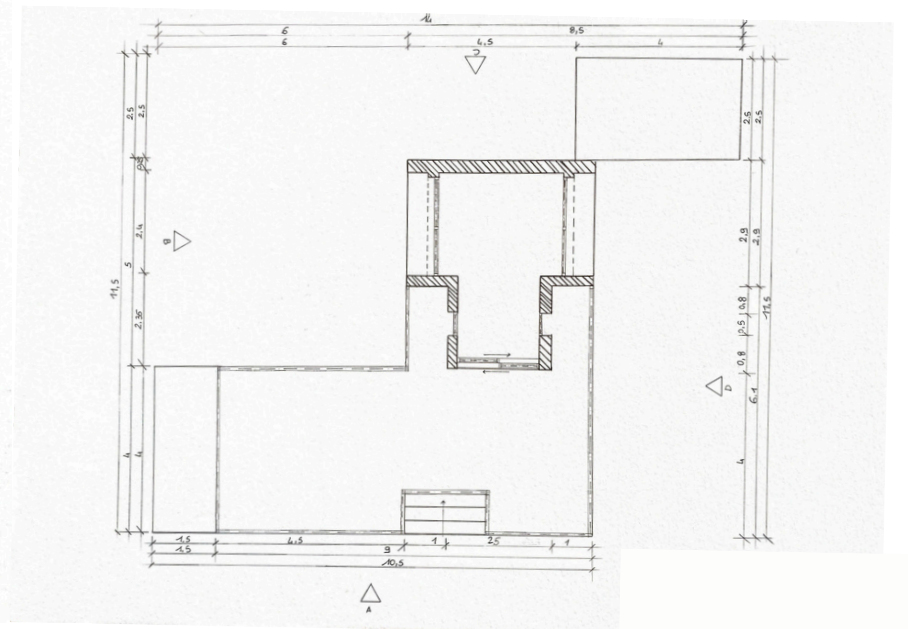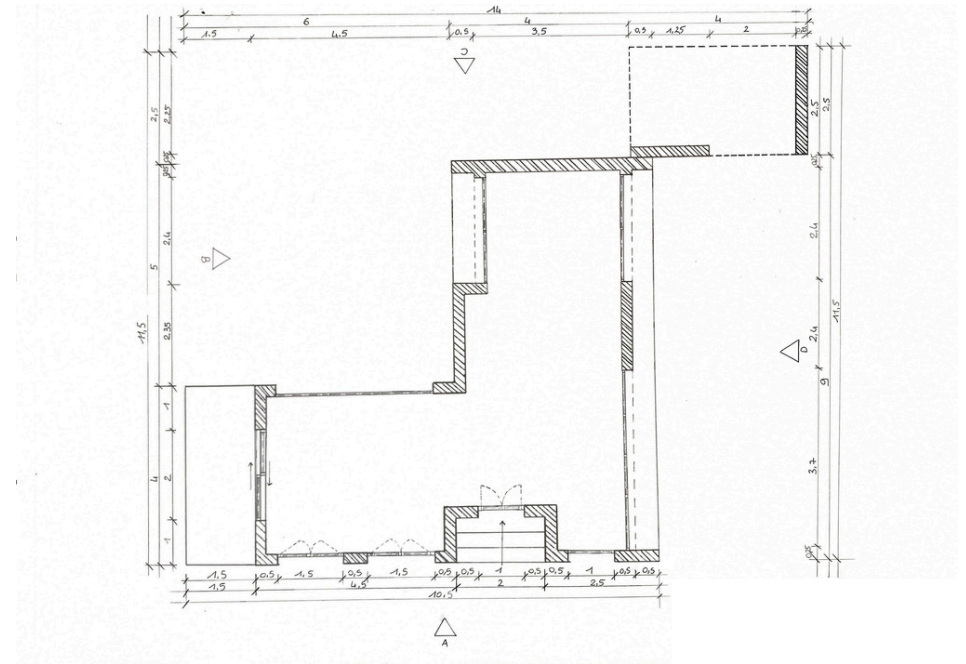


06

TRAVAUX PLASTIQUES & EXPÉRIMENTATIONS

Dessins

projets scolaires
année 2025

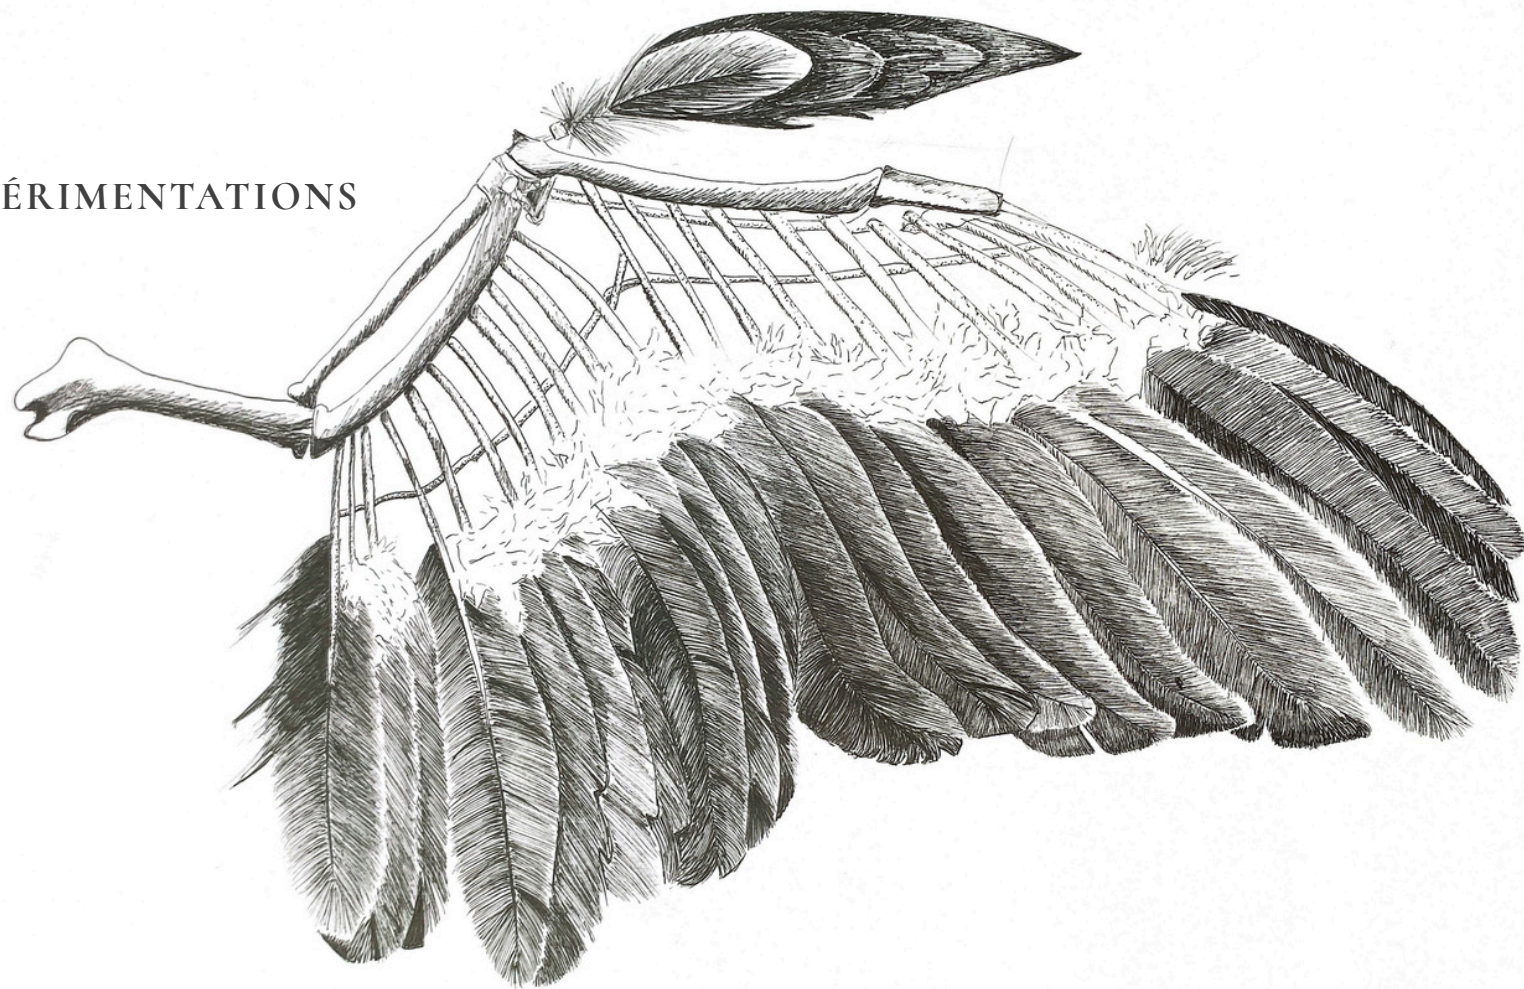

AUX CRAYONS GRIS


AUX FEUTRES TECHNIQUES

06

TRAVAUX PLASTIQUES & EXPÉRIMENTATIONS

Dessins

projets scolaires
années 2025/2026

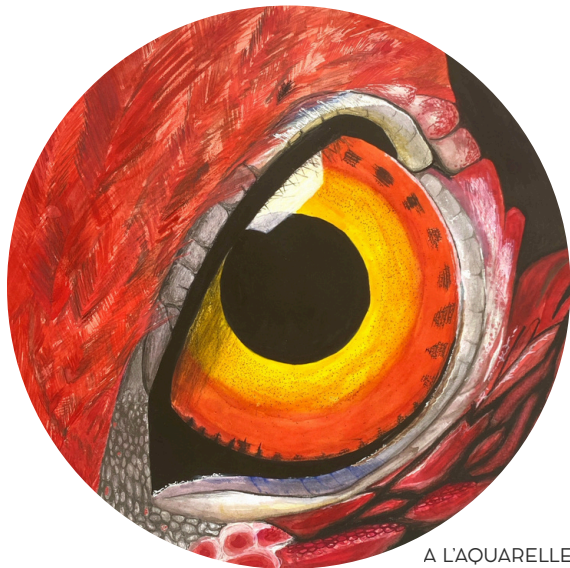

A L'AQUARELLE

AUX CRAYONS GRIS



AU FUSAIN

